


PUNTOS GEOREFERENCIADOS (COORDENADAS UTM ZONA 19 N)				
FACTOR ESCALA COMBINADO = 0.9996432290145				
VERTICE	X	Y	MATERIALIZACION	FECHA
PG-1	559,082.860	2,043,582.064	CLAVO TOPOGRAFICO	27/04/2018
PG-2	559,188.265	2,043,510.442	CLAVO TOPOGRAFICO	27/04/2018
VINCULACION A LA RED GEODESICA DE LA JI				
REP JI	EPOCA DE REFERENCIA			FECHA
SPED	2016.434			D.J.158, año 2016
COORDENADAS GEOGRAFICAS				
CORS VINCULADA	LATITUD	LONGITUD	VINCULACION	FECHA
RDHI	18°35'52.69384"N	68°43'05.95587"W	SPED	20/12/2016
Método de Levantamiento: los PGs y el levantamiento parcelario se realizó en RTK en tiempo real con un Rover Trimble R8.				

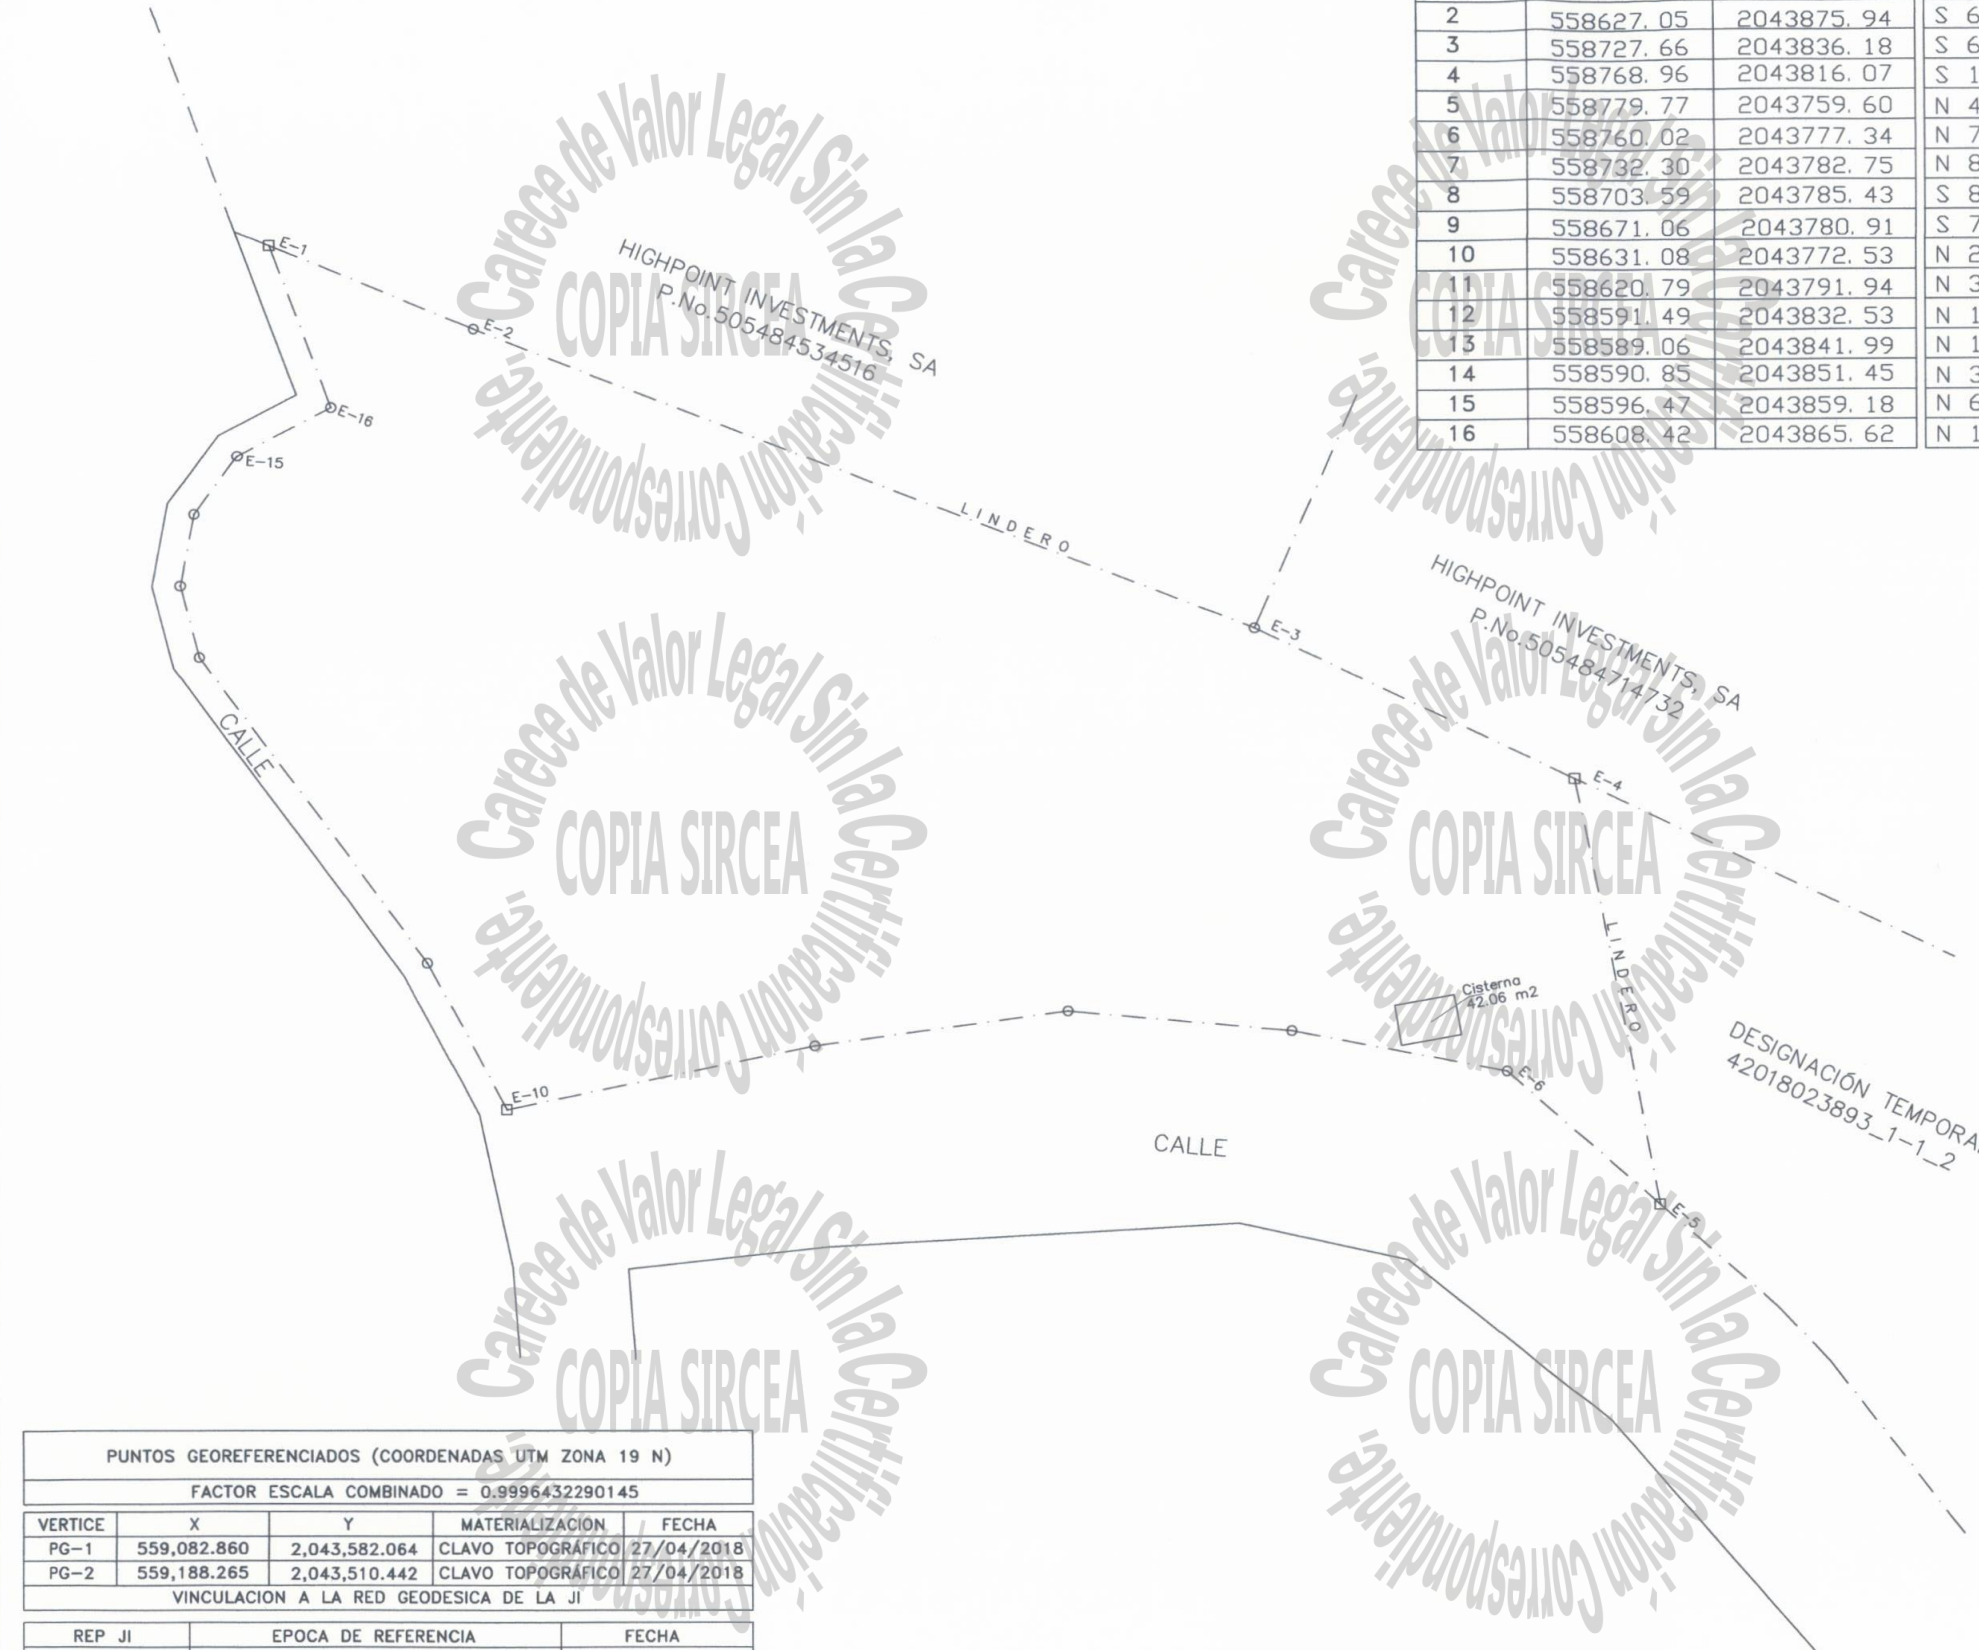

PROYECCION UTM ZONA 19 NORTE			
FACTOR UTM = 0.9996432290145			
VERTICE	X	Y	RUMBO
1	558600.65	2043886.97	S 67°-18' E
2	558627.05	2043875.94	S 68°-26' E
3	558727.66	2043836.18	S 64°-02' E
4	558768.96	2043816.07	S 10°-50' E
5	558779.77	2043759.60	N 48°-04' W
6	558760.02	2043777.34	N 78°-58' W
7	558732.30	2043782.75	N 84°-39' W
8	558703.59	2043785.43	S 82°-05' W
9	558671.06	2043780.91	S 78°-10' W
10	558631.08	2043772.53	N 27°-55' W
11	558620.79	2043791.94	N 35°-50' W
12	558591.49	2043832.53	N 14°-23' W
13	558589.06	2043841.99	N 10°-44' E
14	558590.85	2043851.45	N 36°-00' E
15	558596.47	2043859.18	N 61°-40' E
16	558608.42	2043865.62	N 19°-59' W

27/05/2019 04:30 PM

4A59B7F73F6C417984

03305587

REPUBLICA DOMINICANA PODER JUDICIAL JURISDICCION INMOBILIARIA DIRECCION REGIONAL DE MENSURAS CATASTRALES DEPARTAMENTO ESTE	
PLANO INDIVIDUAL	
OPERACION: SUBDIVISION	
DESIGNACION CATASTRAL POSICIONAL: DCP 505483687149	
DESIGNACIÓN CATASTRAL DE ORIGEN: DESIGNACIÓN TEMPORAL 42018023893_1_1 DISTRITO CATASTRAL No.: DESIGNACIÓN TEMPORAL: 42018023893_1-1_1	
PROVINCIA: LA ALTAGRACIA	
MUNICIPIO: HIGUEY	
SECCION: JINA JARAGUA	
LUGAR: JUANILLO	
REFERENCIAS DE UBICACIÓN: DESDE HIGUEY TOMAR LA CARRETERA PUNTA CANA-JUANILLO HASTA COMPLEJO TURISTICO CAP CANA, DENTRO DEL COMPLEJO TOMAR LA CALLE BOULEVARD CENTRAL EN DIRECCIÓN NORTE-SUR HASTA LA CALLE POR DONDE SE ACCESA AL SCAPE PARK AT CAP CANA. LOS INMUEBLES EN CUESTIÓN SE ENCUENTRAN AL SUR DE SCAPE PARK AT CAP CANA.	
SUPERFICIE A REGISTRAR PARCELA: 12,130.07 m2	ESCALA : 1: 1,000
OBSERVACIONES: "Dentro del inmueble en cuestión se encuentra y se puede visualizar en Google Earth un camino interno, el cual es exclusivo de Cap Cana, s.a."	No. LAMINA 5 9
Certifico haber realizado el trabajo en el terreno conforme a lo dispuesto en el Reglamento General de Mensuras Catastrales MARCOS ANT. BALBI MENDOZA 25951 NOMBRE DEL PROFESIONAL CODIA:	De conformidad con lo dispuesto en el Reglamento General de Mensuras Catastrales FECHA Y FIRMA DEL DIRECTOR DIRECCION REGIONAL DE MENSURAS CATASTRALES DEPARTAMENTO ESTE