
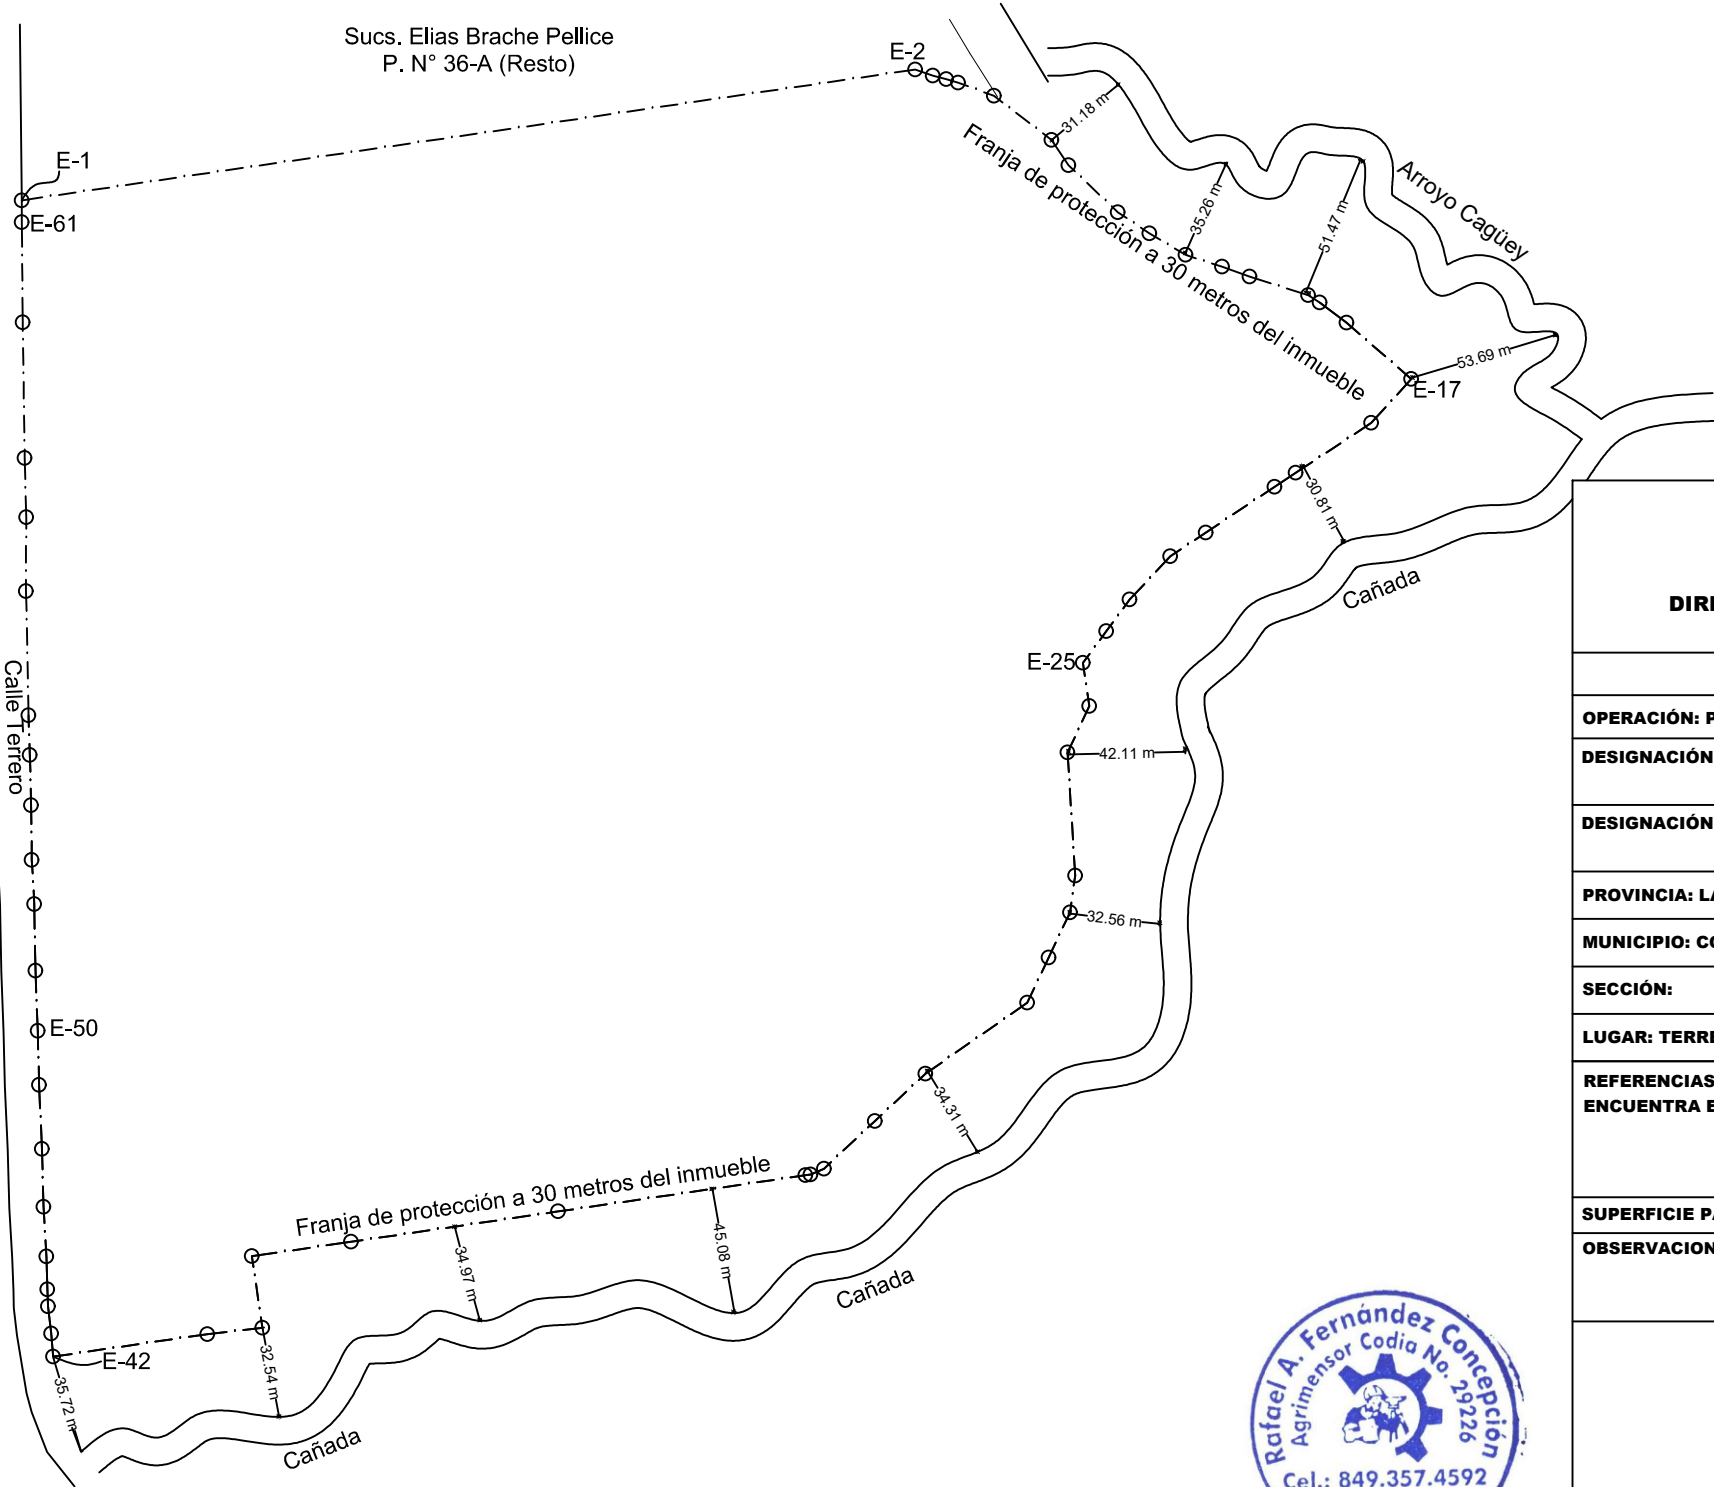


COORDENADAS UTM ZONA 19 NORTE				
EST.	x	y	RUMBO	DIST.
1	339035.87	2124260.34	N81°40'E	325.90 m
2	339358.34	2124307.53	S70°52'E	6.71 m
3	339364.68	2124305.33	S75°46'E	5.01 m
4	339369.54	2124304.10	S73°12'E	4.38 m
5	339373.73	2124302.83	S69°39'E	13.83 m
6	339386.70	2124298.02	S52°36'E	26.23 m
7	339407.53	2124282.09	S33°57'E	10.92 m
8	339413.63	2124273.03	S46°17'E	24.62 m
9	339431.42	2124256.02	S56°08'E	13.69 m
10	339442.79	2124248.39	S59°20'E	15.22 m
11	339455.88	2124240.63	S72°03'E	13.76 m
12	339468.97	2124236.39	S70°04'E	10.61 m
13	339478.95	2124232.77	S72°25'E	22.10 m
14	339500.01	2124226.09	S57°19'E	4.95 m
15	339504.18	2124223.42	S53°16'E	12.13 m
16	339513.91	2124216.16	S49°03'E	30.95 m
17	339537.28	2124195.88	S42°14'W	21.43 m
18	339522.87	2124180.01	S56°37'W	32.74 m
19	339495.54	2124162.00	S56°31'W	9.13 m
20	339487.92	2124156.96	S56°19'W	29.81 m
21	339463.11	2124140.43	S56°19'W	15.42 m
22	339450.28	2124131.88	S43°11'W	21.32 m
23	339435.69	2124116.33	S36°17'W	14.22 m
24	339427.27	2124104.86	S36°40'W	14.14 m
25	339418.83	2124093.52	S08°20'E	15.85 m
26	339421.12	2124077.84	S25°09'W	18.48 m
27	339413.27	2124061.11	S03°31'E	44.48 m
28	339416.00	2124016.71	S08°01'W	13.44 m
29	339414.12	2124003.41	S25°22'W	18.03 m
30	339406.40	2123987.12	S25°22'W	18.03 m
31	339398.68	2123970.83	S55°07'W	44.72 m
32	339362.00	2123945.24	S46°53'W	25.06 m
33	339343.71	2123928.12	S46°53'W	25.06 m
34	339325.42	2123910.99	S66°26'W	5.32 m
35	339320.54	2123908.86	S81°40'W	1.86 m
36	339318.70	2123908.59	S81°40'W	90.17 m
37	339229.49	2123895.53	S81°40'W	75.60 m
38	339154.68	2123884.59	S81°40'W	36.09 m
39	339118.97	2123879.36	S08°20'E	26.08 m
40	339122.75	2123853.55	S83°29'W	20.01 m
41	339102.87	2123851.28	S81°40'W	56.27 m
42	339047.19	2123843.13	N04°34'W	8.31 m
43	339046.53	2123851.42	N06°36'W	9.90 m
44	339045.39	2123861.25	N02°01'W	6.16 m
45	339045.17	2123867.41	N01°42'W	11.87 m
46	339044.82	2123879.28	N03°26'W	17.91 m
47	339043.75	2123897.15	N01°30'W	21.00 m
48	339043.20	2123918.14	N02°33'W	23.12 m
49	339042.17	2123941.24	N01°24'W	19.48 m
50	339041.69	2123960.71	N02°13'W	21.71 m
51	339040.85	2123982.41	N01°02'W	24.04 m
52	339040.42	2124006.45	N03°09'W	15.96 m
53	339039.54	2124022.38	N00°38'W	19.69 m
54	339039.32	2124042.07	N01°33'W	18.13 m
55	339038.83	2124060.19	N01°59'W	14.29 m
56	339038.34	2124074.47	N01°06'W	44.88 m
57	339037.47	2124119.35	N00°02'E	26.63 m
58	339037.49	2124145.98	N01°20'W	21.34 m
59	339036.99	2124167.31	N00°52'W	49.05 m
60	339036.24	2124216.35	N00°28'W	36.10 m
61	339035.95	2124252.45	N00°35'W	7.89 m

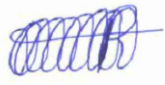

Nota: El método de medición para los vértices de la(s) parcela(s) fue el GNSS RTK y estación total y para los PG el GNSS RTK.

REPÚBLICA DOMINICANA PODER JUDICIAL JURISDICCIÓN INMOBILIARIA DIRECCIÓN REGIONAL DE MENSURAS CATASTRALES DEPARTAMENTO NORTE	
PLANO GENERAL	
OPERACIÓN: PLANO CATASTRAL	
DESIGNACIÓN CATASTRAL DE ORIGEN No (s): P. N° 36-A D.C. 05	
DESIGNACIÓN TEMPORAL No (s):	
PROVINCIA: LA VEGA	
MUNICIPIO: CONCEPCIÓN DE LA VEGA	
SECCIÓN:	
LUGAR: TERRERO	
REFERENCIAS DE UBICACIÓN: EN LA PROLONGACIÓN AV. MONSEÑOR PANAL SE ENCUENTRA EL INMUEBLE.	
SUPERFICIE PARCELA: 156,222.44 m²	ESCALA: 1:2,500
OBSERVACIONES: YERMO	No. de Lámina 1 / 1
DESIGNACIÓN CATASTRAL POSICIONAL:	
Certifico haber realizado el trabajo en el terreno conforme a lo dispuesto en el Reglamento General de Mensuras Catastrales  Agrimensor Rafael Antonio Fernández Concepción CODIA: 29226	De conformidad a lo dispuesto en el Reglamento General de Mensuras Catastrales Fecha y firma del Director Dirección Regional de Mensuras Catastrales Departamento Norte